
Level 3 | Experiment lab and teaching room

Current powered bench layout, perimeter services and occupied-space allowances

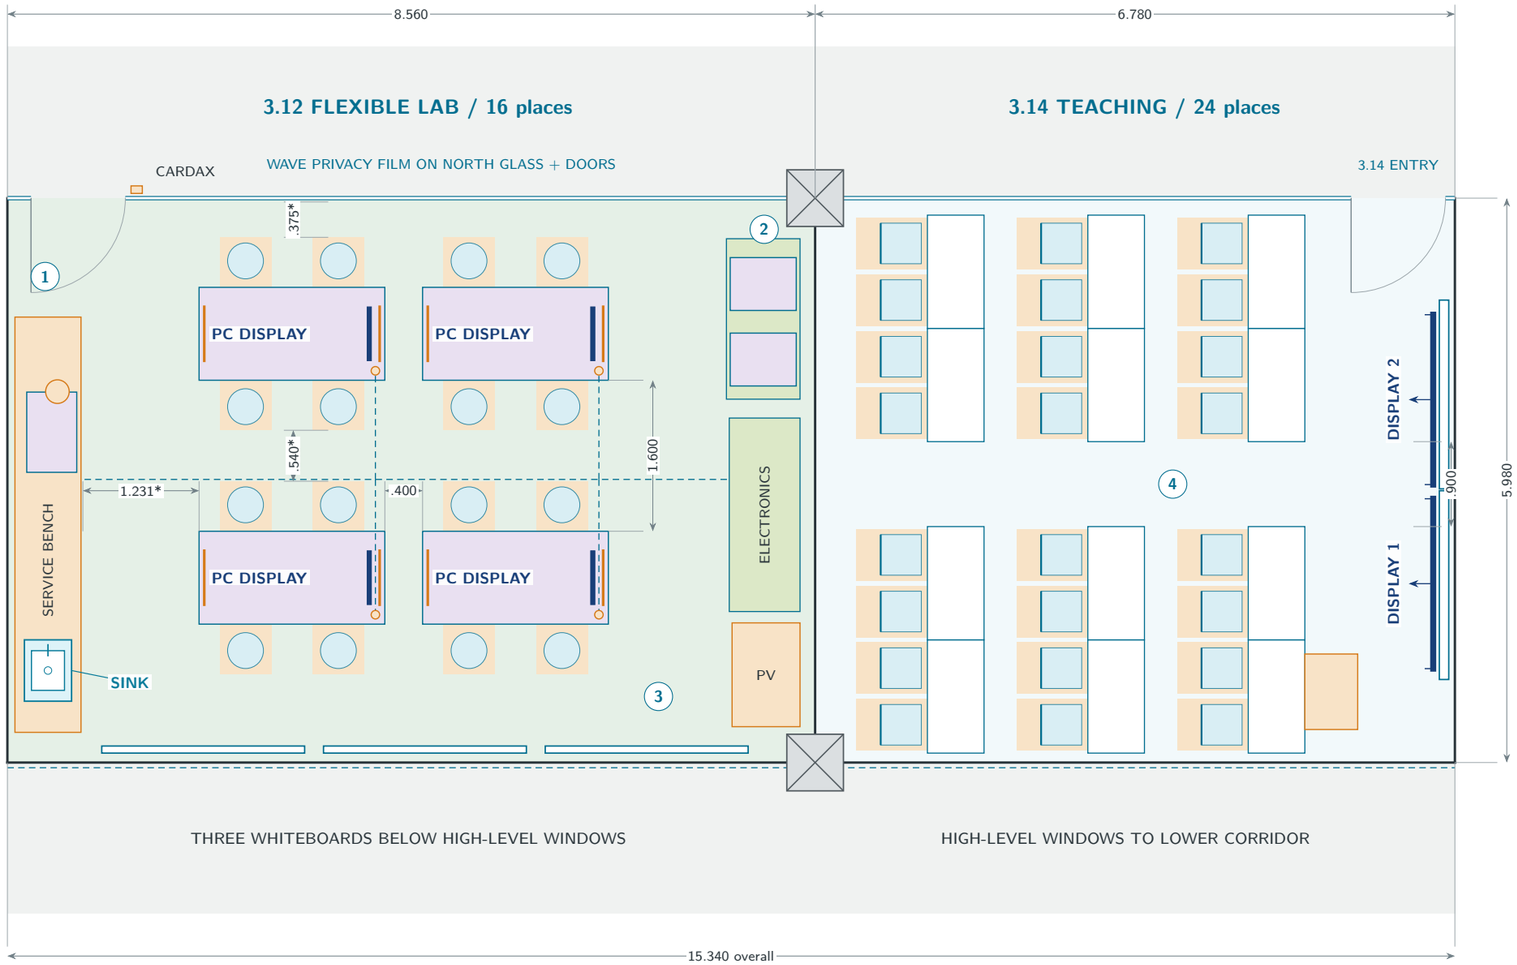

1 / Flexible lab

Four 1969 x 984 mm benches, 900 mm high, with two stools on each long side: 16 places. Each has one PC display at its east end, four outlets under the ends and overhead supply. No centre service rail.

Perimeter services

West: 4.40 m service bench, 700 mm deep, with sink and solder station / local extraction. South: three 2.15 m whiteboards below clerestory windows. East: PV demonstration equipment, electronics cupboard and exactly two enclosed 3D printers.

2 / Storage and printers

Electronics cupboard: 2050 mm wide x 750 mm deep, with 650 mm shelves. Printer bench: 1700 x 780 mm. Shown closed; open doors and active work areas share adjacent circulation space.

3 / Revised lab clearances

The bench-edge gap is 1.600 m: the south pair moves 100 mm towards the whiteboards. With 530 mm occupied projections, 540 mm remains between seated rows. The north rear gap stays 375 mm; the south occupied envelope is 936 mm from the wall (671 mm from the board tray). The 400 mm short-end gap is for plug access. * Outer clearances: about 1.231 m. Tight occupied gaps are not circulation routes.

4 / Teaching room

Twelve 1200 x 600 mm desks provide 24 places facing east. The rear north desk group is reinstated. The 1.00 m entrance moves to the east end of the north frontage, opening inward into the front aisle. The 900 mm central aisle remains. The lectern touches the east edge of the front south desk. Two east-wall 1.80 m displays have a 150 mm gap.

Current design, beyond the earlier plan

The lab and teaching fronts, including both north doors, have wave-pattern privacy film between 0.75 and 1.85 m above the floor, strongest in the centre. Above and below remain clear. Four east-end PCs retain the walkthrough swivel and keyboard-tray detail.

Drawing conventions

Dark-blue DISPLAY bars and arrows show the teaching screens and viewing direction. White outlines are boards; blue basin marks the SINK. Crosses mark columns. Amber = occupied allowance; dashed blue = overhead power or high glazing. Dimensions remain conceptual.

MODEL SCALE / metres

0 1 5