
Level 1 | Laboratory detail

Current 1.22 experiment layout and 1.23 teaching layout

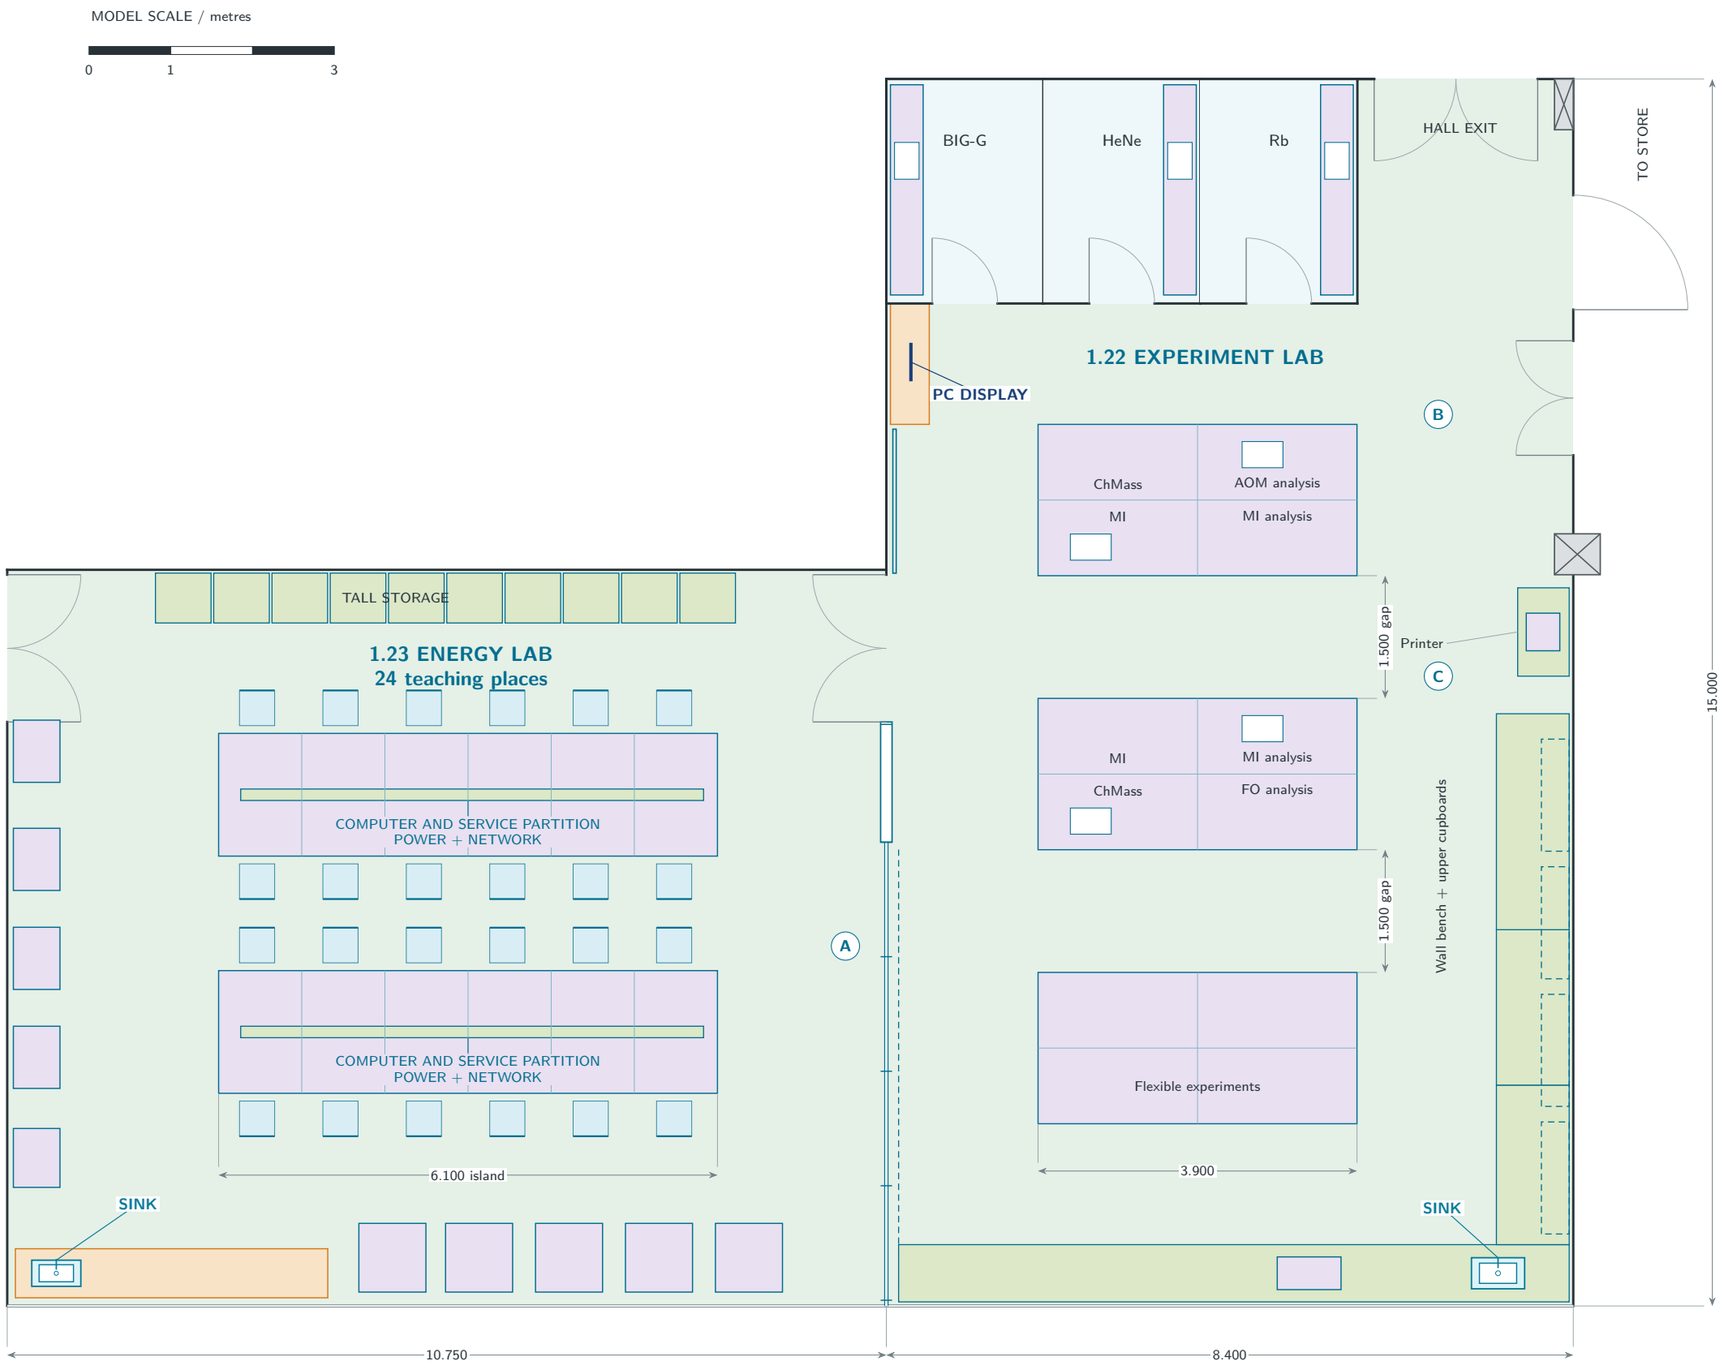

A / Shared wall

Clear full-height glazing with curtain is shown. The 1.47 m bay immediately beside the connecting doors remains a permanent whiteboard on both faces to 2.20 m. See sheet 05 for the smart-glass and solid-wall alternatives.

B / Current connecting doors

The seminar-to-lab exit in the current walkthrough is 1.400 m overall, with two 700 mm leaves at p = 10.40–11.80 m. The 1.400 m width is the confirmed current design. The store door is also 1.400 m; the upper hall exit is 2.000 m.

C / Shared column and printer

One 560 x 500 mm column spans the 1.22 / 1.21 partition south of the emergency exit. Its footprint follows the earlier 1.22 drawing. The 630 x 1080 mm printer bench sits immediately south. East-wall cupboards are dashed overhead; the south bench retains the apparatus and sink.

Benches and services

1.22: three 3.900 x 1.850 m islands with 1.500 m gaps. BIG-G workstation display and wall whiteboard remain on the west side.

1.23: six seats per long side of each island, 24 total. The green strips are computer and service partitions providing power and network connections. Shared-wall whiteboards remain white.

Drawing key

- Experiment bench / equipment
- Storage / cabinetry
- SINK / basin
- DEMONSTRATOR STATION
- Illustrative occupied space
- Structural column
- DISPLAY / arrow faces into room
- Full-height glazing
- Overhead / high-level element