
Level 1 | Coordinated floor plan

Rooms 1.21, 1.22 and 1.23 with store and upper hallway

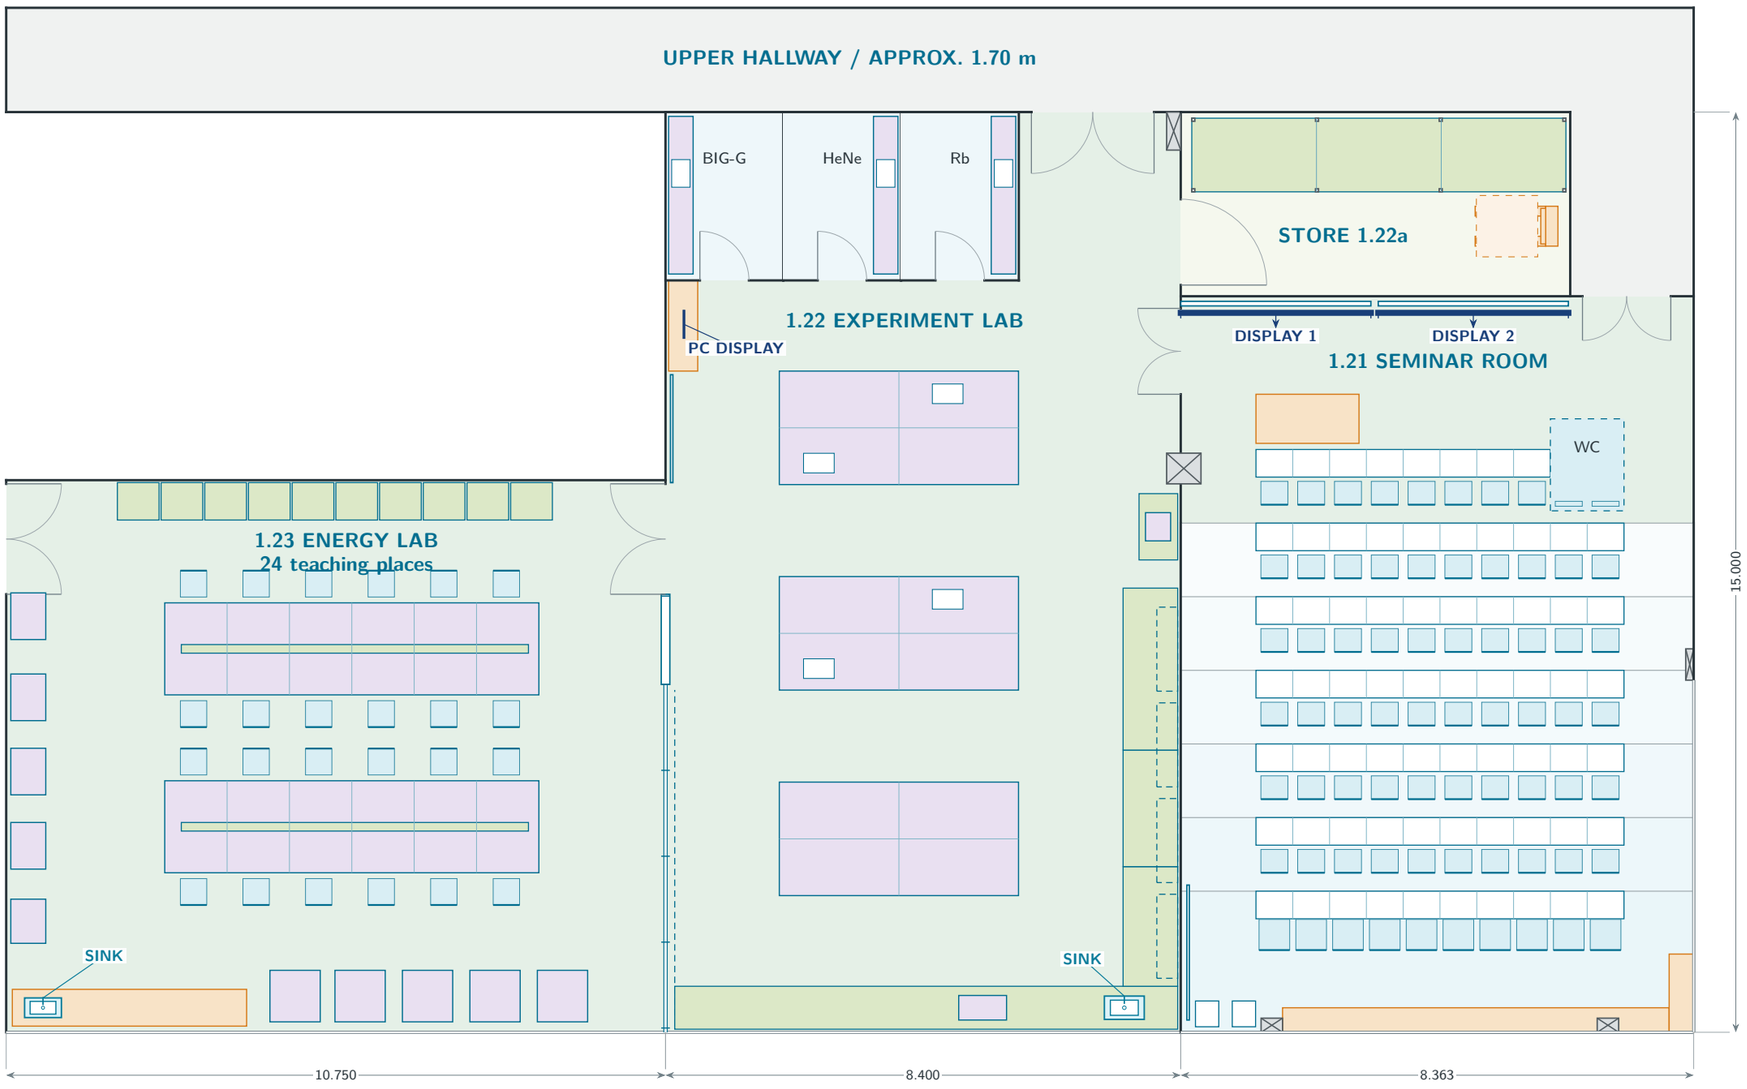

MODEL SCALE / metres

0 1 5

Basis and orientation

Dimensions are in metres and follow the model. The upper hallway is at the top of every Level 1 sheet. Wall thicknesses and perimeter alignments remain conceptual.

What this sheet records

The current local walkthrough is the design source. Enlarged labs appear on sheet 03; the seminar room and store on sheet 04; shared-wall options on sheet 05.

1.21 seminar room

North boundary at 11.998 m, moved 500 mm south to enlarge the store. Six main desk rows at 1.200 m pitch plus one rear desk row. 68 desk seats, with room for another 10 as overflow rear seating. Wheelchair bay shown with two fold-downs stowed; see sheet 04.

1.22 experiment lab

Three 3.900 x 1.850 m bench islands, retained BIG-G / HeNe / Rb rooms, south and east perimeter benching. One 560 x 500 mm column spans the 1.22 / 1.21 partition south of the emergency exit. The printer station lies south of this column.

1.23 energy lab

Two 6.100 x 1.500 m islands with green computer and service partitions for power and network, plus 24 teaching places. Perimeter equipment and north-wall storage are retained. Clear glazing plus curtain is the default at the shared wall.

Drawing key

- Experiment bench / equipment
- Storage / cabinetry
- SINK / basin
- DEMONSTRATOR STATION
- Illustrative occupied space
- Structural column
- DISPLAY / arrow faces into room
- Full-height glazing
- Overhead / high-level element