
Level 1 | Seminar room and store

Desk-aligned tiers, rear platform, current rack and widened store door

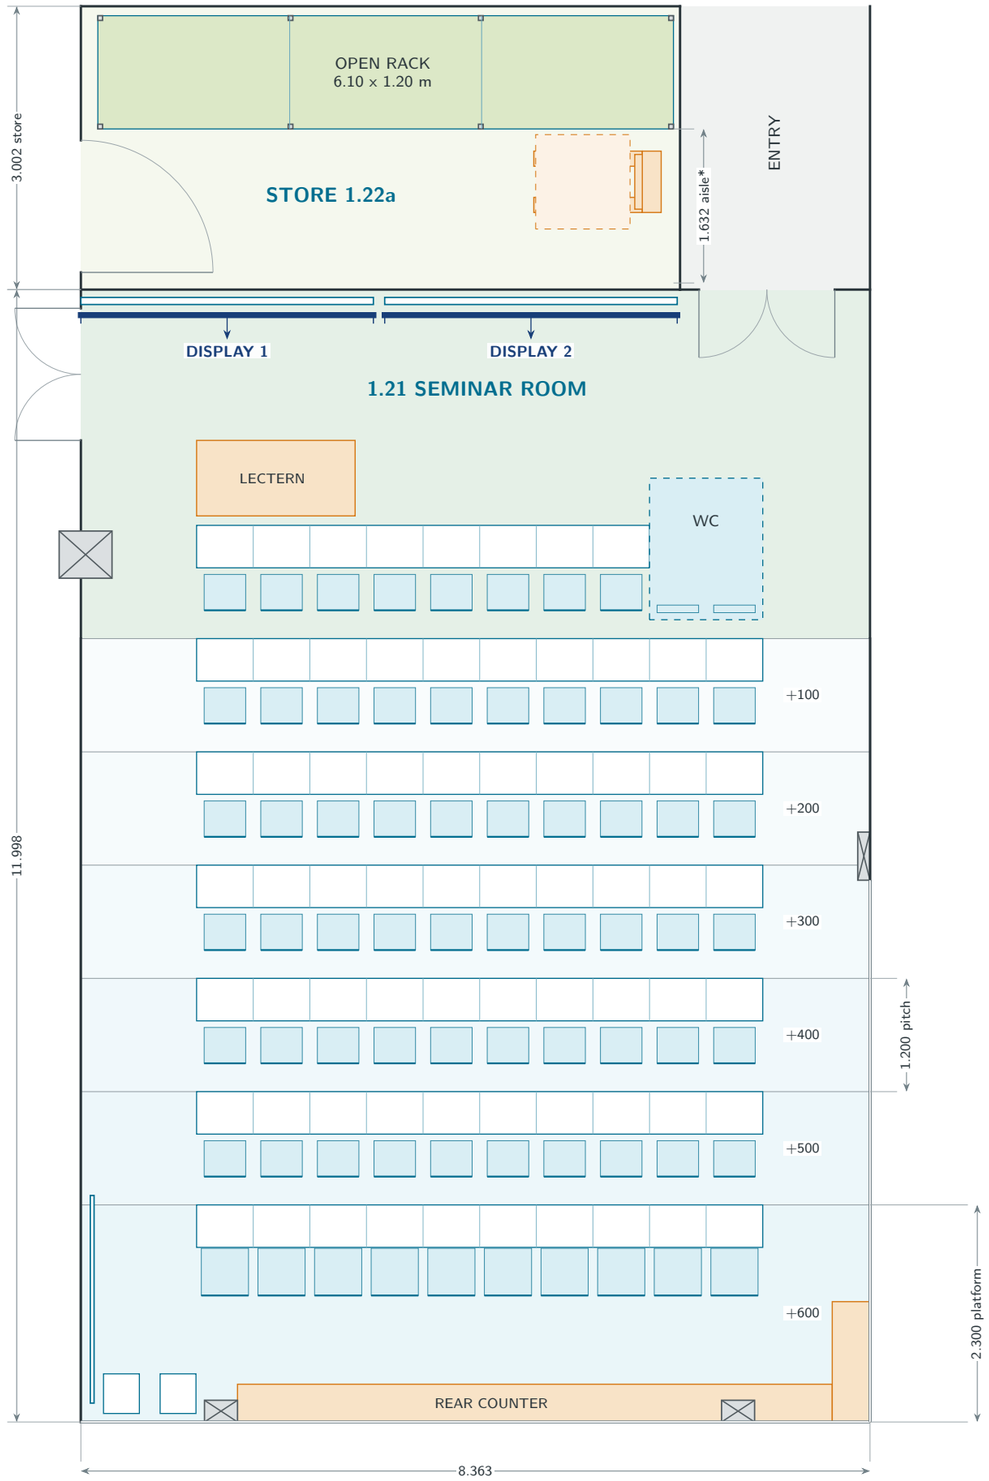

Seating and access

68 desk seats = 8 in the first row + five rows of 10 + 10 at the rear desk. Two fold-downs can occupy the wheelchair bay (70 seats). With the fold-downs stowed, the illustrated occupied mode has 68 desk users + one wheelchair user (69 people). Room for another 10 as overflow rear seating (see inset); 78 seats plus the wheelchair user in that mode.

Tier and rear-platform geometry

Six 100 mm rises reach the +600 mm rear platform. Each raised tier begins at its desk front; the first row stays at floor level. Desk depth is 450 mm and the row pitch is 1.200 m. The rear platform is 2.300 m deep. Ceiling is 3.000 m above level floor, leaving 2.400 m above the rear platform.


Store / * nominal aisle before parked equipment

The single north rack is 6.10 m long x 1.20 m deep and meets the east inside wall face. The rack-to-south-wall clear aisle is 1.632 m before the parked lift/load is included. Store door: 1.400 m, south hinge retained. The hand lift and 1 m load are illustrative; the parked load reduces the local aisle to about 0.57 m.


Teaching and rear fittings

Two 3.10 m teaching screens, with a 120 mm gap, cover paired over/under boards at the north wall. Permanent rear whiteboard on the west wall. Rear counter is 400 mm deep with a short east return; two five-chair stacks remain at the west end.

Longitudinal section / schematic furniture at model positions

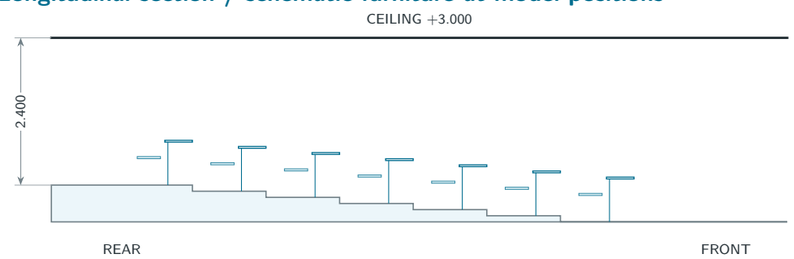

Optional overflow / rear plan inset at 1:100

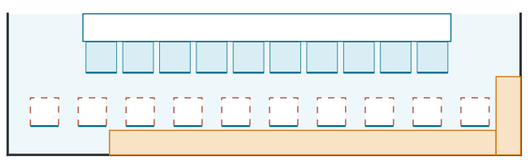

Ten extra loose chairs

Dashed red chairs have 700 mm-high seats, no desks, and extend into both rear aisles at 780 mm centres. Stacks are removed in this mode. The 79-person occupied scenario is illustrative; rear circulation is restricted.

