
Level 2 | Teaching, meeting and store

Room 2.28: partition, current desk runs, lectern and AV fittings

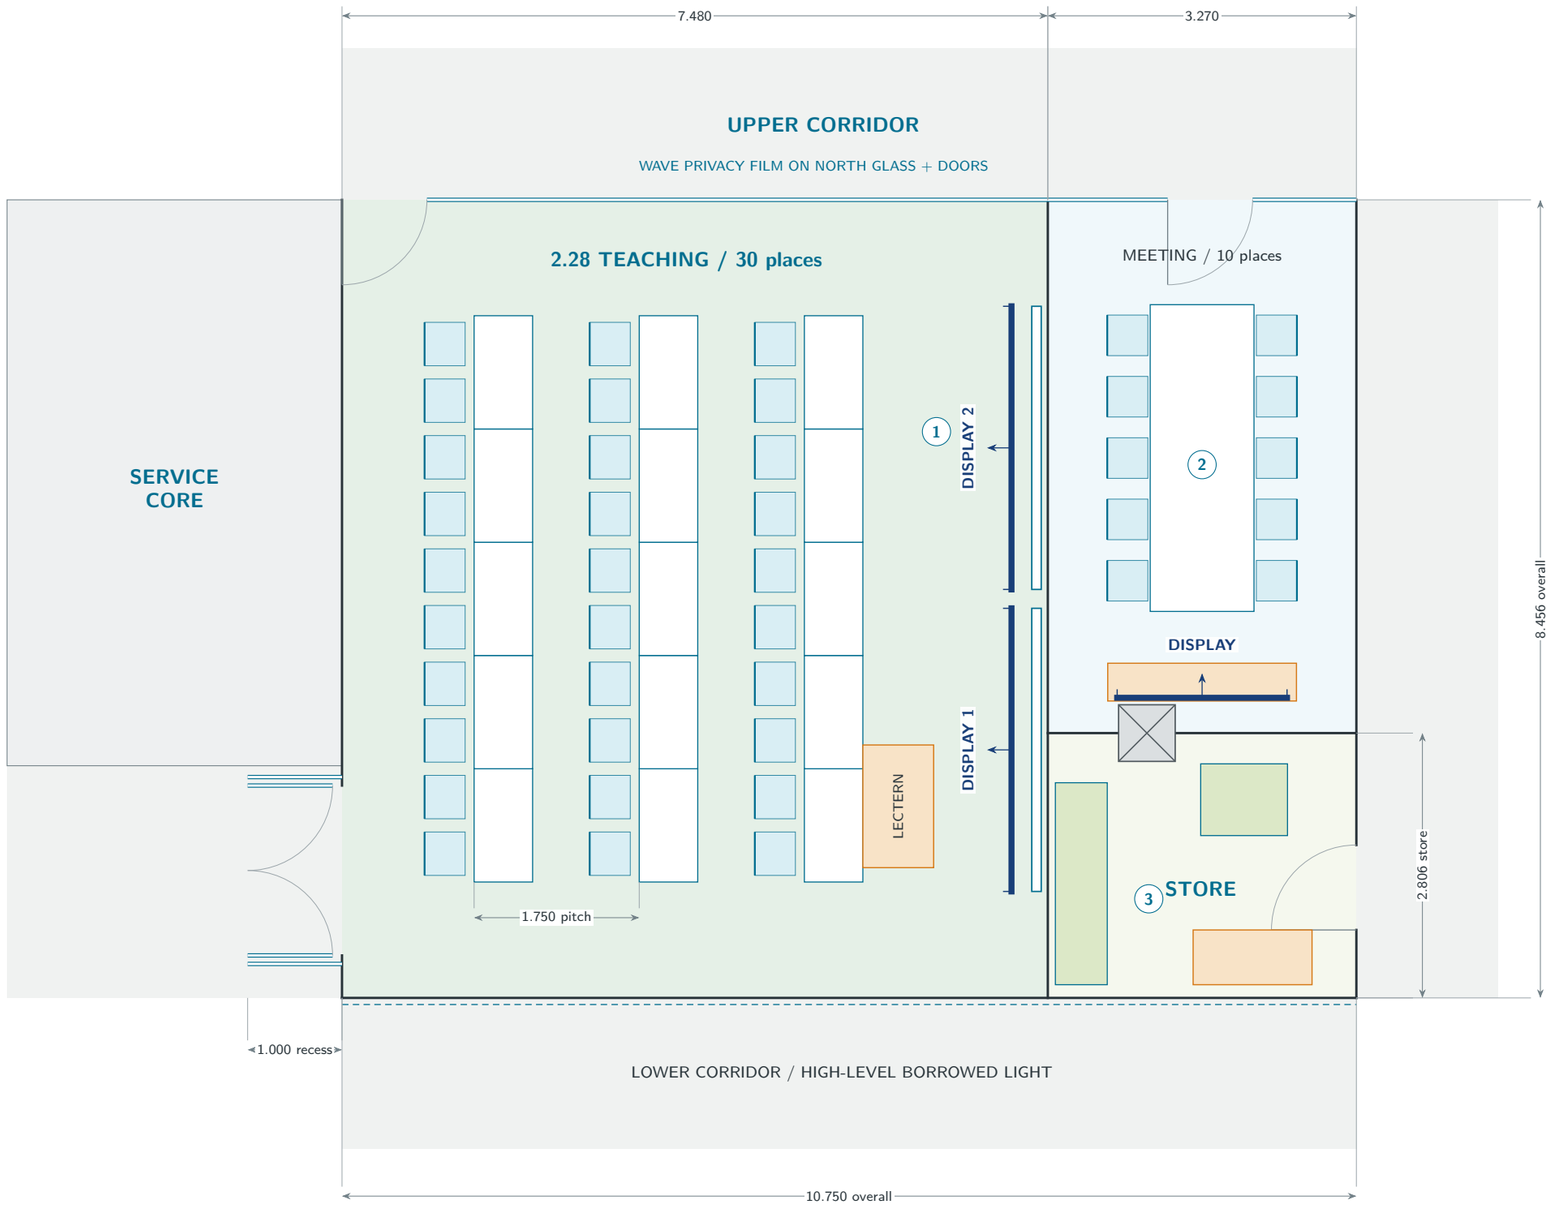

MODEL SCALE / metres

0 1 5

1 / Teaching room

Three 6.00 m desk runs at 1.750 m pitch provide 30 places. Fifteen 1200 x 620 mm desks face the east partition. The 750 x 1300 mm lectern is at its current north-shifted position, clear of the south side aisle.

Teaching wall

Two 3.00 m-wide screens cover two pairs of counter-sliding whiteboard panels. Dashed south-wall glazing is high-level borrowed light. North glass and its doors carry wave-pattern privacy film at 0.75–1.85 m, strongest at the centre. The west entry is recessed 1.00 m; both 900 mm leaves swing east within the recess.

2 / Meeting room

3.25 x 1.10 m table with ten chairs. AV console and display sit on the north side of the return partition. The 600 mm column stays centred on the return-wall line.

3 / Store

L-shaped partition retains a 2.806 m-deep store with east access, west tall cupboard, south worktop and equipment storage.

Drawing key

- Experiment bench / equipment
- Storage / cabinetry
- SINK / basin
- DEMONSTRATOR STATION
- Illustrative occupied space
- Structural column
- DISPLAY / arrow faces into room
- Full-height glazing
- Overhead / high-level element

Plan basis

Geometry follows the current Level 2 walkthrough, including the updated lectern. Desks, chairs and door swings are shown at model size. Dimensions are in metres.